


VÍA LOCAL PREFERENCIAL

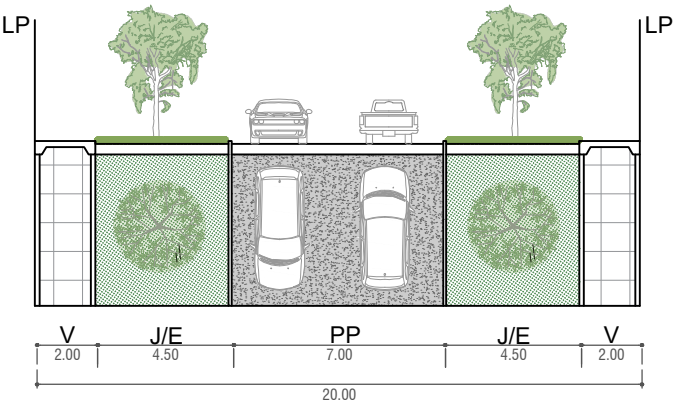

AVENIDA DE LAS ARTES NORTE (20 m)

Sector: 3,4  
Subsector: A, B, C | A, B, C  
Tramo: Av. Boulevard de Surco - Av. San Borja Norte

- NOTAS:**
- 1. En caso de que cualquier proyecto contemple modificaciones a dichas secciones, estas deberán adecuarse a la normativa vigente, en concordancia con el Reglamento Nacional de Tránsito, el Manual de Dispositivos de Control del Tránsito Automotor para Calles y Carreteras y la Ordenanza 341-MML y modificatorias.
  - 2. El nombre de la vía fue aprobada mediante Acuerdo de Concejo N.º 123, de fecha 30-04-2001.

**LEYENDA**

- LP = LÍMITE DE PROPIEDAD  
V = VEREDA  
J/E = JARDÍN / ESTACIONAMIENTO  
VC = VÍA CICLISTA  
SC = SEPARADOR CENTRAL  
PP = PISTA PRINCIPAL  
PS = PISTA SECUNDARIA  
J = JARDÍN  
E = ESTACIONAMIENTO  
SL = SEPARADOR LATERAL  
TP = PISTA EXCLUSIVA DE TRANSPORTE PÚBLICO



ORDENANZA QUE APRUEBA LA CLASIFICACIÓN Y SECCIONES VIALES DEL DISTRITO DE SAN BORJA DE LAS VÍAS LOCALES DEL DISTRITO DE SAN BORJA

Descripción: SECCIONES VIALES DEL DISTRITO DE SAN BORJA

Vía: AVENIDA DE LAS ARTES NORTE

Escala: 1/250

Distrito: SAN BORJA

Año: 2026

Lámina:

VLP-AV-07