


VÍA LOCAL PREFERENCIAL

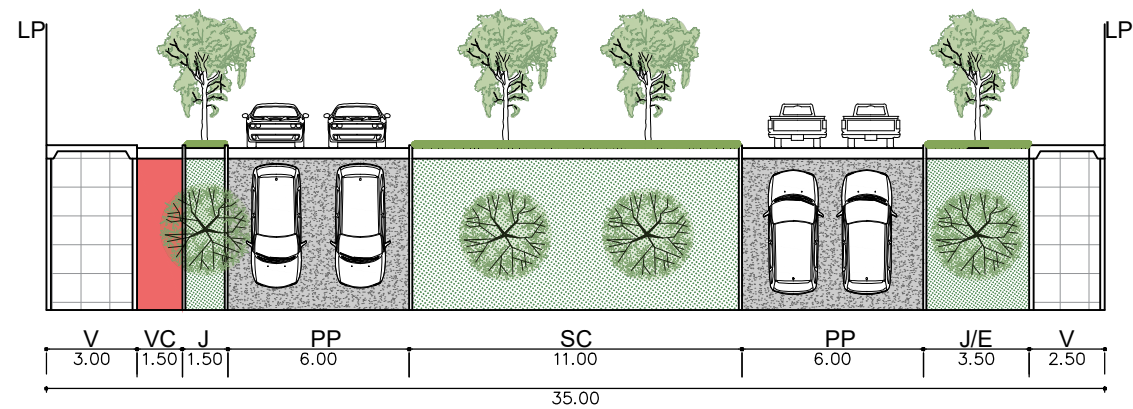

AVENIDA TNTE. ALEJANDRO VELASCO
ASTETE (35 m)

Sector: 12

Subsector: C

Tramo: Av. Esmeralda – Av. Cmdte. Juan Bielovucic Cavalier

NOTAS:

- En caso de que cualquier proyecto contemple modificaciones a dichas secciones, estas deberán adecuarse a la normativa vigente, en concordancia con el Reglamento Nacional de Tránsito, el Manual de Dispositivos de Control del Tránsito Automotor para Calles y Carreteras y la Ordenanza 341-MML y modificatorias.
- El nombre de la vía fue aprobada mediante Acuerdo de Concejo N.º 100, de fecha 19-04-2001.

LEYENDA

- LP = LÍMITE DE PROPIEDAD
V = VEREDA
J/E = JARDÍN / ESTACIONAMIENTO
VC = VÍA CICLISTA
SC = SEPARADOR CENTRAL
PP = PISTA PRINCIPAL
PS = PISTA SECUNDARIA
J = JARDÍN
E = ESTACIONAMIENTO
SL = SEPARADOR LATERAL
TP = PISTA EXCLUSIVA DE TRANSPORTE PÚBLICO



ORDENANZA QUE APRUEBA LA CLASIFICACIÓN Y
SECCIONES VIALES DEL DISTRITO DE SAN BORJA DE
LAS VÍAS LOCALES DEL DISTRITO DE SAN BORJA

Descripción: SECCIONES VIALES DEL DISTRITO DE SAN BORJA

Vía: AVENIDA TNTE. ALEJANDRO VELASCO ASTETE

Escala:
1/250

Distrito:
SAN BORJA

Año:
2026

Lámina:

VLP-AV-18A