


VÍA LOCAL SECUNDARIA

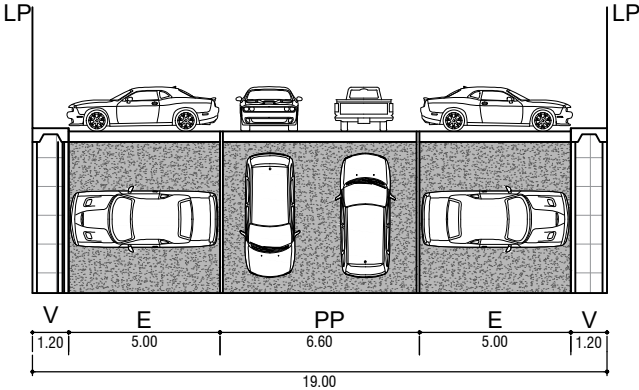

ALAMEDA FRANCISCO GARCIA CALDERON
REY (19 m)

Sector: 1
Subsector: A
Tramo: Psj. Juan Gonzalo Rose - Zona de estacionamiento

- NOTAS:**
- 1. En caso de que cualquier proyecto contemple modificaciones a dichas secciones, estas deberán adecuarse a la normativa vigente, en concordancia con el Reglamento Nacional de Tránsito, el Manual de Dispositivos de Control del Tránsito Automotor para Calles y Carreteras y la Ordenanza 341-MML y modificatorias.
 - 2. El nombre de la vía fue aprobada mediante Acuerdo de Concejo N.º 125, de fecha 30-04-2001.

LEYENDA

- LP = LÍMITE DE PROPIEDAD
V = VEREDA
J/E = JARDÍN / ESTACIONAMIENTO
VC = VÍA CICLISTA
SC = SEPARADOR CENTRAL
PP = PISTA PRINCIPAL
PS = PISTA SECUNDARIA
J = JARDÍN
E = ESTACIONAMIENTO
SL = SEPARADOR LATERAL
TP = PISTA EXCLUSIVA DE TRANSPORTE PÚBLICO



ORDENANZA QUE APRUEBA LA CLASIFICACIÓN Y
SECCIONES VIALES DE LAS VÍAS LOCALES DEL
DISTRITO DE SAN BORJA

Descripción: SECCIONES VIALES DEL DISTRITO DE SAN BORJA

Vía: ALAMEDA FRANCISCO GARCIA CALDERON REY

Escala:
1/250

Distrito:
SAN BORJA

Año:
2026

Lámina:

VLS-AL-10D