


VÍA LOCAL SECUNDARIA

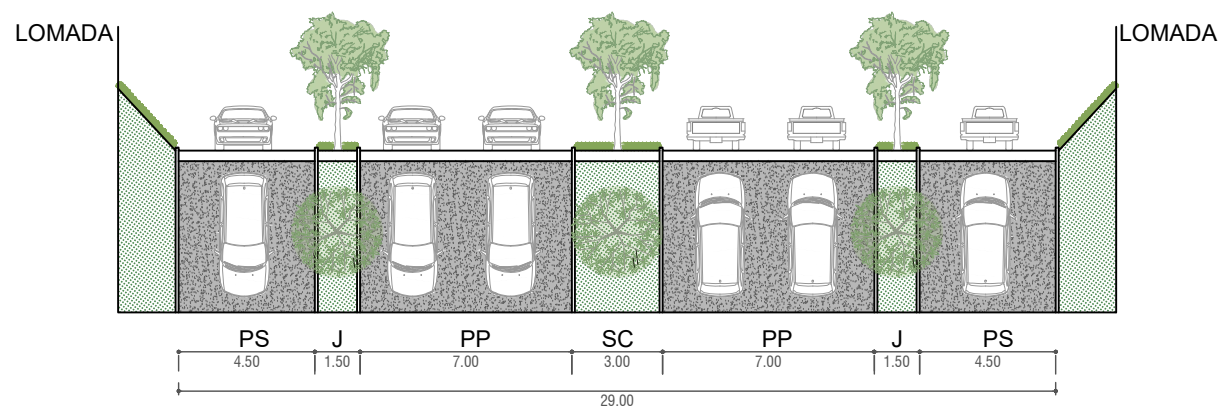

AVENIDA MAYOR MARKO JARA SCHENONE (29 m)

Sector: 12
Subsector: C
Tramo: Av. Panamericana Sur - Alam. Picaflores

- NOTAS:**
- 1. En caso de que cualquier proyecto contemple modificaciones a dichas secciones, estas deberán adecuarse a la normativa vigente, en concordancia con el Reglamento Nacional de Tránsito, el Manual de Dispositivos de Control del Tránsito Automotor para Calles y Carreteras y la Ordenanza 341-MML y modificatorias.
 - 2. El nombre de la vía fue aprobada mediante Acuerdo de Concejo N.º 100, de fecha 19-04-2001.

LEYENDA

- LP = LÍMITE DE PROPIEDAD
- V = VEREDA
- J/E = JARDÍN / ESTACIONAMIENTO
- VC = VÍA CICLISTA
- SC = SEPARADOR CENTRAL
- PP = PISTA PRINCIPAL
- PS = PISTA SECUNDARIA
- J = JARDÍN
- E = ESTACIONAMIENTO
- SL = SEPARADOR LATERAL
- TP = PISTA EXCLUSIVA DE TRANSPORTE PÚBLICO



ORDENANZA QUE APRUEBA LA CLASIFICACIÓN Y SECCIONES VIALES DE LAS VÍAS LOCALES DEL DISTRITO DE SAN BORJA

Descripción: SECCIONES VIALES DEL DISTRITO DE SAN BORJA

Vía: AVENIDA MAYOR MARKO JARA SCHENONE

Escala: 1/250

Distrito: SAN BORJA

Año: 2026

Lámina:

VLS-AV-01