


VÍA LOCAL PREFERENCIAL

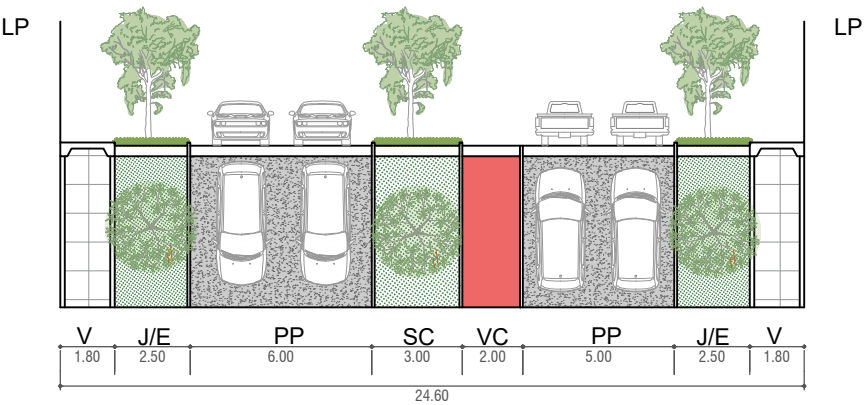

AVENIDA BUENA VISTA (24.60 m)

Sector: 12
Subsector: C
Tramo: Av. Primavera - Ca. Crl. Juan Valer Sandoval

- NOTAS:**
- 1. En caso de que cualquier proyecto contemple modificaciones a dichas secciones, estas deberán adecuarse a la normativa vigente, en concordancia con el Reglamento Nacional de Tránsito, el Manual de Dispositivos de Control del Tránsito Automotor para Calles y Carreteras y la Ordenanza 341-MML y modificatorias.
 - 2. El nombre de la vía fue aprobada mediante Acuerdo de Concejo N.º 100, de fecha 19-04-2001 y Acuerdo de Concejo N.º 115, de fecha 30-04-2001.

LEYENDA

- LP = LÍMITE DE PROPIEDAD
V = VEREDA
J/E = JARDÍN / ESTACIONAMIENTO
VC = VÍA CICLISTA
SC = SEPARADOR CENTRAL
PP = PISTA PRINCIPAL
PS = PISTA SECUNDARIA
J = JARDÍN
E = ESTACIONAMIENTO
SL = SEPARADOR LATERAL
TP = PISTA EXCLUSIVA DE TRANSPORTE PÚBLICO



ORDENANZA QUE APRUEBA LA CLASIFICACIÓN Y SECCIONES VIALES DEL DISTRITO DE SAN BORJA DE LAS VÍAS LOCALES DEL DISTRITO DE SAN BORJA

Descripción: SECCIONES VIALES DEL DISTRITO DE SAN BORJA

Vía: AVENIDA BUENA VISTA

Escala: 1/250

Distrito: SAN BORJA

Año: 2026

Lámina:

VLP-AV-03A