


VÍA LOCAL PREFERENCIAL

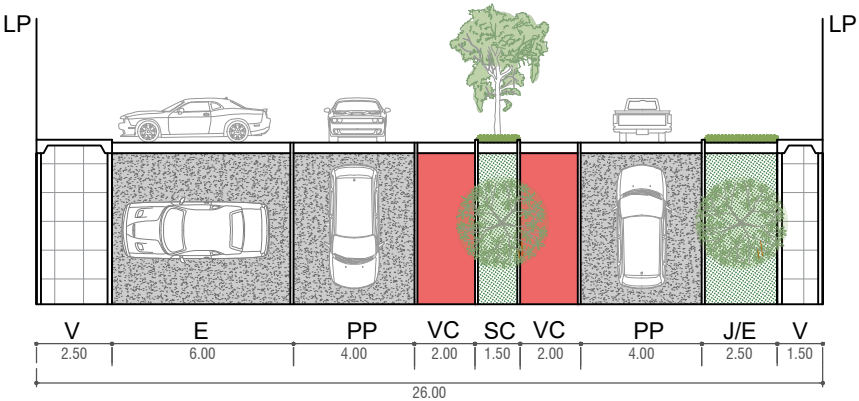

AVENIDA RICARDO MALACHOWSKI
KULISICZ (21.50 m)

Sector: 10

Subsector: A, B

Tramo: Ca. Roque Vargas Prada - Av. Jose Galvez Barrenechea

NOTAS:

- 1. En caso de que cualquier proyecto contemple modificaciones a dichas secciones, estas deberán adecuarse a la normativa vigente, en concordancia con el Reglamento Nacional de Tránsito, el Manual de Dispositivos de Control del Tránsito Automotor para Calles y Carreteras y la Ordenanza 341-MML y modificatorias.
- 2. El nombre de la vía fue aprobada mediante Acuerdo de Concejo N.º 161, de fecha 30-05-2001.

LEYENDA

- LP = LÍMITE DE PROPIEDAD
- V = VEREDA
- J/E = JARDÍN / ESTACIONAMIENTO
- VC = VÍA CICLISTA
- SC = SEPARADOR CENTRAL
- PP = PISTA PRINCIPAL
- PS = PISTA SECUNDARIA
- J = JARDÍN
- E = ESTACIONAMIENTO
- SL = SEPARADOR LATERAL
- TP = PISTA EXCLUSIVA DE TRANSPORTE PÚBLICO



ORDENANZA QUE APRUEBA LA CLASIFICACIÓN Y SECCIONES VIALES DEL DISTRITO DE SAN BORJA DE LAS VÍAS LOCALES DEL DISTRITO DE SAN BORJA

Descripción: SECCIONES VIALES DEL DISTRITO DE SAN BORJA

Vía: AVENIDA RICARDO MALACHOWSKI KULISICZ

Escala: 1/250

Distrito: SAN BORJA

Año: 2026

VLP-AV-17B