


VÍA LOCAL PREFERENCIAL

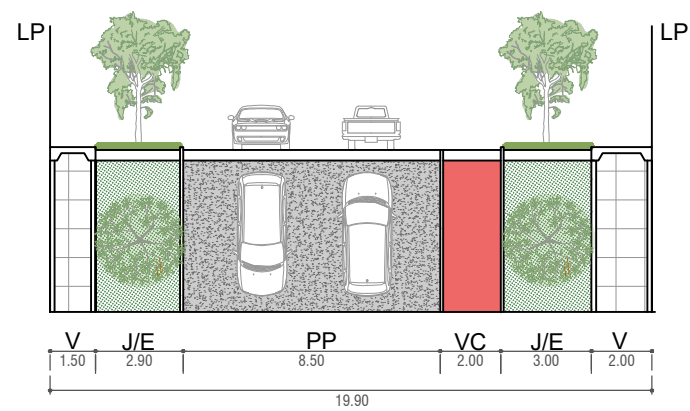

CALLE DE LAS LETRAS (19.90 m)

Sector: 1
Subsector: A
Tramo: Av. De la Poesia - Av. Del Aire

- NOTAS:**
- 1. En caso de que cualquier proyecto contemple modificaciones a dichas secciones, estas deberán adecuarse a la normativa vigente, en concordancia con el Reglamento Nacional de Tránsito, el Manual de Dispositivos de Control del Tránsito Automotor para Calles y Carreteras y la Ordenanza 341-MML y modificatorias.
 - 2. El nombre de la vía fue aprobada mediante Acuerdo de Concejo N.º 125, de fecha 30-04-2001, Acuerdo de Concejo N.º 163, de fecha 30-05-2001 y Acuerdo de Concejo N.º 165, de fecha 30-05-2001.

LEYENDA

- LP = LÍMITE DE PROPIEDAD
V = VEREDA
J/E = JARDÍN / ESTACIONAMIENTO
VC = VÍA CICLISTA
SC = SEPARADOR CENTRAL
PP = PISTA PRINCIPAL
PS = PISTA SECUNDARIA
J = JARDÍN
E = ESTACIONAMIENTO
SL = SEPARADOR LATERAL
TP = PISTA EXCLUSIVA DE TRANSPORTE PÚBLICO



ORDENANZA QUE APRUEBA LA CLASIFICACIÓN Y SECCIONES VIALES DE LAS VÍAS LOCALES DEL DISTRITO DE SAN BORJA

Descripción: SECCIONES VIALES DEL DISTRITO DE SAN BORJA

Vía: CALLE DE LAS LETRAS

Escala: 1/250

Distrito: SAN BORJA

Año: 2026

Lámina:

VLP-CA-19B