


VÍA LOCAL PREFERENCIAL

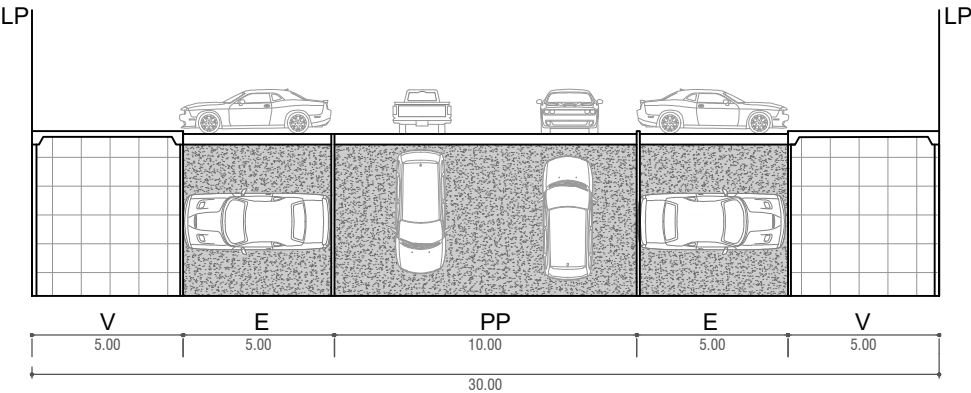

CALLE DEL COMERCIO (30 m)

Sector: 1
Subsector: B
Tramo: Av. De la Arqueología - Av. Aviación

- NOTAS:**
- En caso de que cualquier proyecto contemple modificaciones a dichas secciones, estas deberán adecuarse a la normativa vigente, en concordancia con el Reglamento Nacional de Tránsito, el Manual de Dispositivos de Control del Tránsito Automotor para Calles y Carreteras y la Ordenanza 341-MML y modificatorias.
 - El nombre de la vía fue aprobada mediante Acuerdo de Concejo N.º 170, de fecha 30-05-2001, Acuerdo de Concejo N.º 123, de fecha 30-04-2001, Acuerdo de Concejo N.º 125 de fecha 30-04-2001 y Acuerdo de Concejo N.º 166 de fecha 30-05-2001

LEYENDA

- LP = LÍMITE DE PROPIEDAD
V = VEREDA
J/E = JARDÍN / ESTACIONAMIENTO
VC = VÍA CICLISTA
SC = SEPARADOR CENTRAL
PP = PISTA PRINCIPAL
PS = PISTA SECUNDARIA
J = JARDÍN
E = ESTACIONAMIENTO
SL = SEPARADOR LATERAL
TP = PISTA EXCLUSIVA DE TRANSPORTE PÚBLICO



ORDENANZA QUE APRUEBA LA CLASIFICACIÓN Y SECCIONES VIALES DE LAS VÍAS LOCALES DEL DISTRITO DE SAN BORJA

Descripción: SECCIONES VIALES DEL DISTRITO DE SAN BORJA

Vía: CALLE DEL COMERCIO

Escala: 1/250

Distrito: SAN BORJA

Año: 2026

Lámina:

VLP-CA-21