


VÍA LOCAL SECUNDARIA

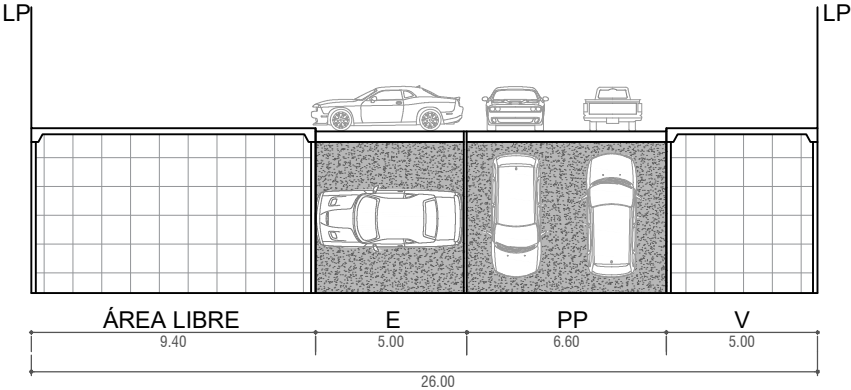

ALAMEDA FRANCISCO GARCIA CALDERON  
REY (26 m)

Sector: 1  
Subsector: A  
Tramo: Psj. Felipe Pardo - Inicio Zona de Estacionamiento

- NOTAS:**
- En caso de que cualquier proyecto contemple modificaciones a dichas secciones, estas deberán adecuarse a la normativa vigente, en concordancia con el Reglamento Nacional de Tránsito, el Manual de Dispositivos de Control del Tránsito Automotor para Calles y Carreteras y la Ordenanza 341-MML y modificatorias.
  - El nombre de la vía fue aprobada mediante Acuerdo de Concejo N.º 125, de fecha 30-04-2001.

**LEYENDA**

- LP = LÍMITE DE PROPIEDAD  
V = VEREDA  
J/E = JARDÍN / ESTACIONAMIENTO  
VC = VÍA CICLISTA  
SC = SEPARADOR CENTRAL  
PP = PISTA PRINCIPAL  
PS = PISTA SECUNDARIA  
J = JARDÍN  
E = ESTACIONAMIENTO  
SL = SEPARADOR LATERAL  
TP = PISTA EXCLUSIVA DE TRANSPORTE PÚBLICO



ORDENANZA QUE APRUEBA LA CLASIFICACIÓN Y  
SECCIONES VIALES DE LAS VÍAS LOCALES DEL  
DISTRITO DE SAN BORJA

Descripción: SECCIONES VIALES DEL DISTRITO DE SAN BORJA

Vía: ALAMEDA FRANCISCO GARCIA CALDERON REY

Escala:  
1/250

Distrito:  
SAN BORJA

Año:  
2026

Lámina:

VLS-AL-10A